
SUBESTACIÓN AÉREA BIPOSTE (SAB) 10 / 0.38 - 0.22 kV (50 kVA y 100 kVA)
MONTAJE ELECTROMECÁNICO NORMALIZADO SEGÚN NORMA DGE / MEM

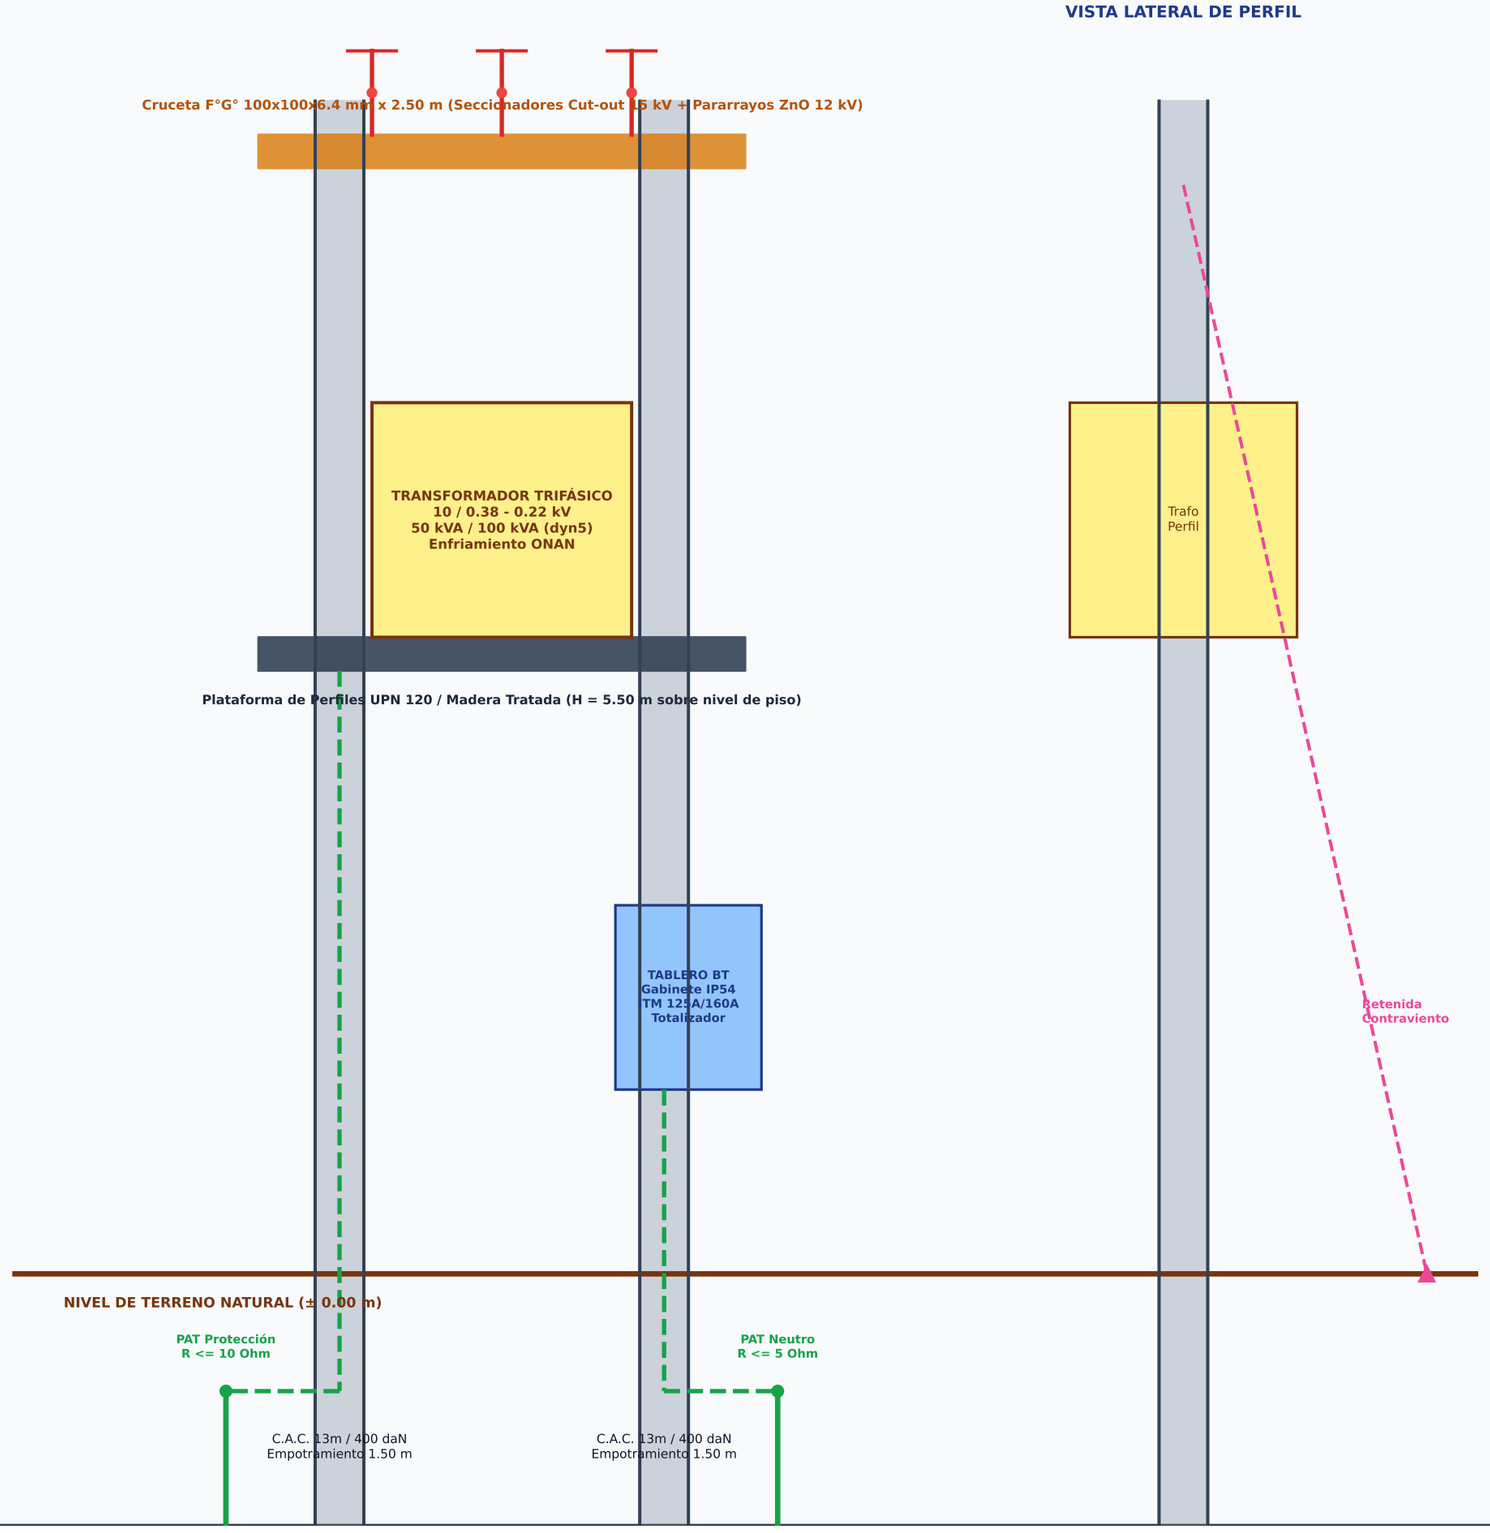

VISTA LATERAL DE PERFIL

ESPECIFICACIONES DE MONTAJE SAB

Postes Principales:	2 x CAC 13m / 400 daN (Norma DGE)
Separación entre Postes:	2.00 m entre ejes
Profundidad Empotramiento:	1.50 m con solado de concreto f'c=140
Plataforma Soporte:	Perfiles de acero galvanizado UPN 120
Transformador Trifásico:	Dyn5, 10 / 0.38-0.22 kV, ONAN
• SED-01 (Jr. Villa Hermosa):	50 kVA / Corriente In = 76.0 A
• SED-02 (Plaza de Armas):	100 kVA / Corriente In = 151.9 A
• SED-03 (Estadio-Piscina):	100 kVA / Corriente In = 151.9 A
Seccionamiento MT:	3 Cut-out 15 kV, 100 A, BIL 110 kV
Protección Sobretensiones:	3 Pararrayos ZnO 12 kV, 10 kA
Fusibles Chicote:	Tipo K (3A para 50kVA, 6A para 100kVA)
Tablero de Distribución BT:	Gabinete intemperie poliéster IP54
Interruptor General Termomagnético:	Regulable (100A para SED-01, 160A para SED-02/03)
Sistema de Puesta a Tierra PAT:	2 pozos verticales independientes:
• PAT-1 Protección (Masas MT):	Varilla Cu 5/8"x2.4m, R <= 10 Ohm
• PAT-2 Servicio (Neutro BT):	Varilla Cu 5/8"x2.4m, R <= 5 Ohm
Distancia entre Pozos PAT:	Minimo 6.0 m de separación

UNIVERSIDAD NACIONAL DEL ALTIPLANO — PUNO
FACULTAD DE INGENIERÍA MECÁNICA ELÉCTRICA (FIME)

ESCUELA PROFESIONAL DE INGENIERÍA MECÁNICA ELÉCTRICA
CURSO: INSTALACIONES ELÉCTRICAS II / REDES ELÉCTRICAS

EXPEDIENTE TÉCNICO: REDES ELÉCTRICAS MCH LIMBANI (200 kW)
DISTRITO DE LIMBANI — SANDIA — PUNO (3,050 m.s.n.m.)

PLANO: DETALLE SUBESTACIÓN AÉREA BIPOSTE (SAB)

PROYECTISTA: Br. Aquiles Taylor Ramos Yapo (Cód. 227368)
DOCENTE: Docente FIME - UNA Puno

FECHA:	ESCALA:	LÁMINA:
Octubre 2026	1 : 50 / 1 : 25	PL-03