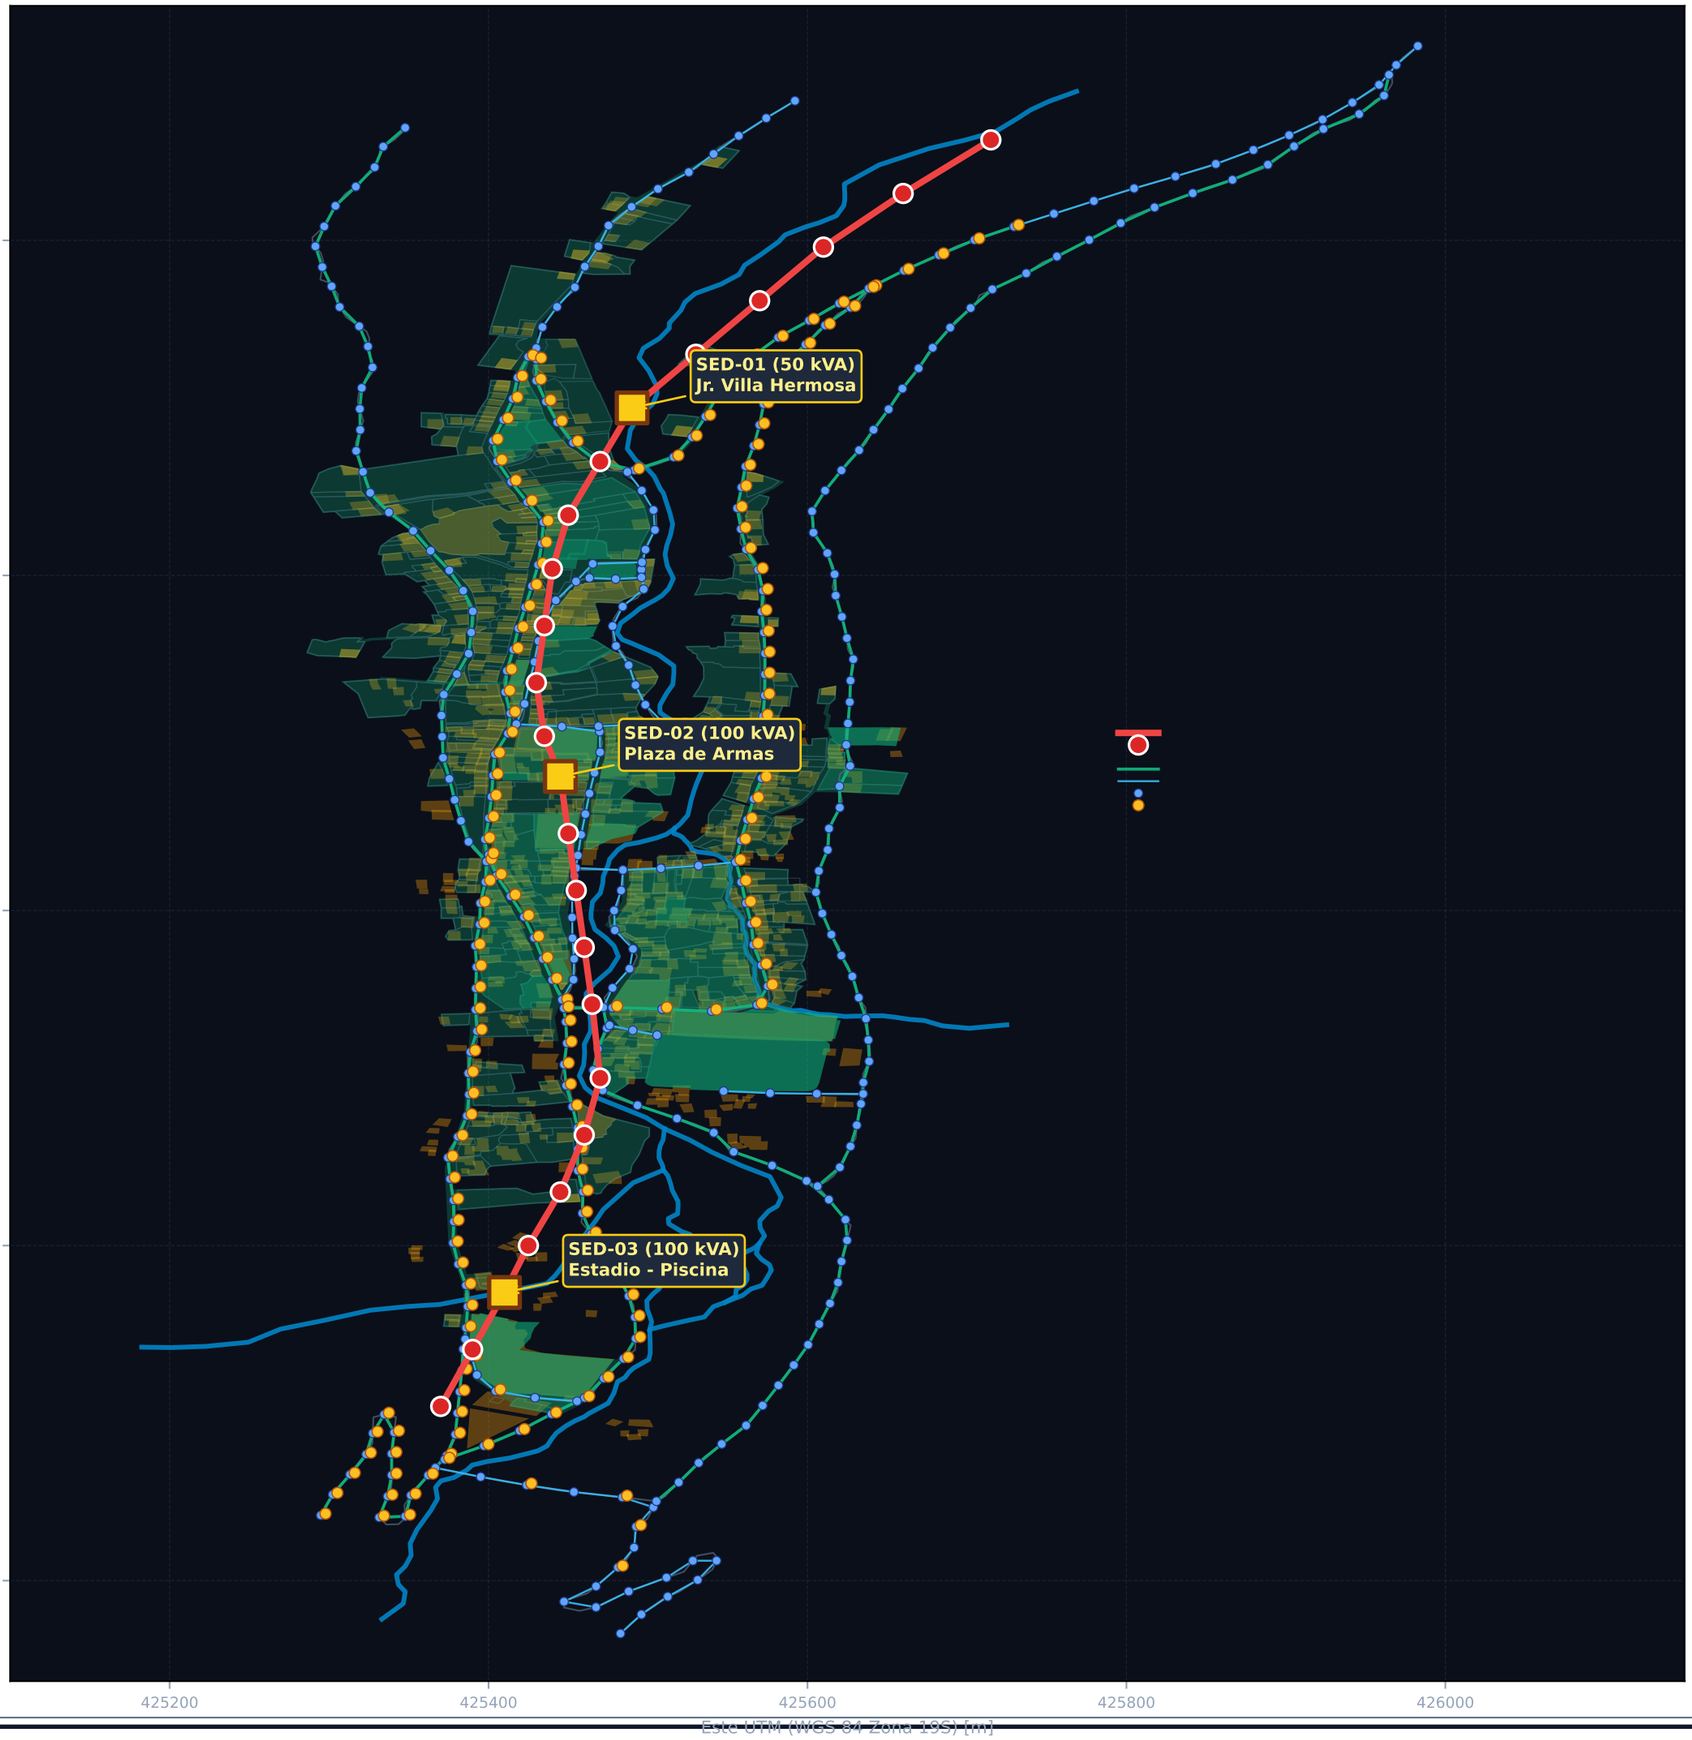


SIMBOLOGÍA ELECTROMECÁNICA

- Línea MT 10 kV (AAAC 35 mm²)
- Poste MT (C.A.C. 12m y 13m)
- Subestación SAB (50 / 100 kVA)
- Red BT Troncal CAAI 3x35+1x16+NA25
- Red BT Derivación CAAI 2x16+1x16+NA25
- Poste BT (C.A.C. 8m y 9m)
- Alumbrado Público LED 50W (165 und)
- Retenida / Anclaje a Tierra
- Río Limbani / Quebradas

RESUMEN TÉCNICO DE REDES

Generación MCH Limbani:	200.0 kW (Michell-Banki, 380 V)
Tensión de Transmisión MT:	10.0 kV (Trifásica, 60 Hz)
Longitud Línea Primaria:	1,967.87 m (1.97 km)
Conductor de Línea MT:	AAAC 35 mm² (Desnudo)
Subestaciones Aéreas SAB:	3 SEDs (Total 250 kVA)
• SED-01 Norte (Jr. V. Hermosa):	50 kVA (142 viviendas)
• SED-02 Centro (Plaza Armas):	100 kVA (348 viviendas)
• SED-03 Sur (Estadio-Piscina):	100 kVA (274 viviendas)
Redes Secundarias BT CAAI:	11,755.60 m (11.76 km)
Total Postería CAC MT / BT:	26 MT / 360 BT (386 postes)
Alumbrado Público LED:	165 luminarias LED 50 W
Demanda Coincidente Total:	181.80 kW (F.C. = 90.9%)
Pérdidas Joule en MT:	0.84% (Excelente eficiencia)

UNIVERSIDAD NACIONAL DEL ALTIPLANO — PUNO
FACULTAD DE INGENIERÍA MECÁNICA ELÉCTRICA (FIME)

ESCUELA PROFESIONAL DE INGENIERÍA MECÁNICA ELÉCTRICA
CURSO: INSTALACIONES ELÉCTRICAS II / REDES ELÉCTRICAS

EXPEDIENTE TÉCNICO: REDES ELÉCTRICAS MCH LIMBANI (200 kW)
DISTRITO DE LIMBANI — SANDIA — PUNO (3,050 m.s.n.m.)

PLANO: REDES ELÉCTRICAS Y CATASTRO URBANO

PROYECTISTA: Br. Aquiles Taylor Ramos Yapo (Cód. 227368)
DOCENTE: Docente FIME - UNA Puno

FECHA:	ESCALA:	LÁMINA:
Octubre 2026	1 : 2500	PL-01