PERFIL LONGITUDINAL TOPOGRÁFICO DE LA LÍNEA PRIMARIA 10 kV — MCH LIMBANI A TERMINAL SUR

Conductor AAAC 35 mm² | Tensión 10 kV | Conductor Catenaria Truxa Flecha Máxima a 35 °C

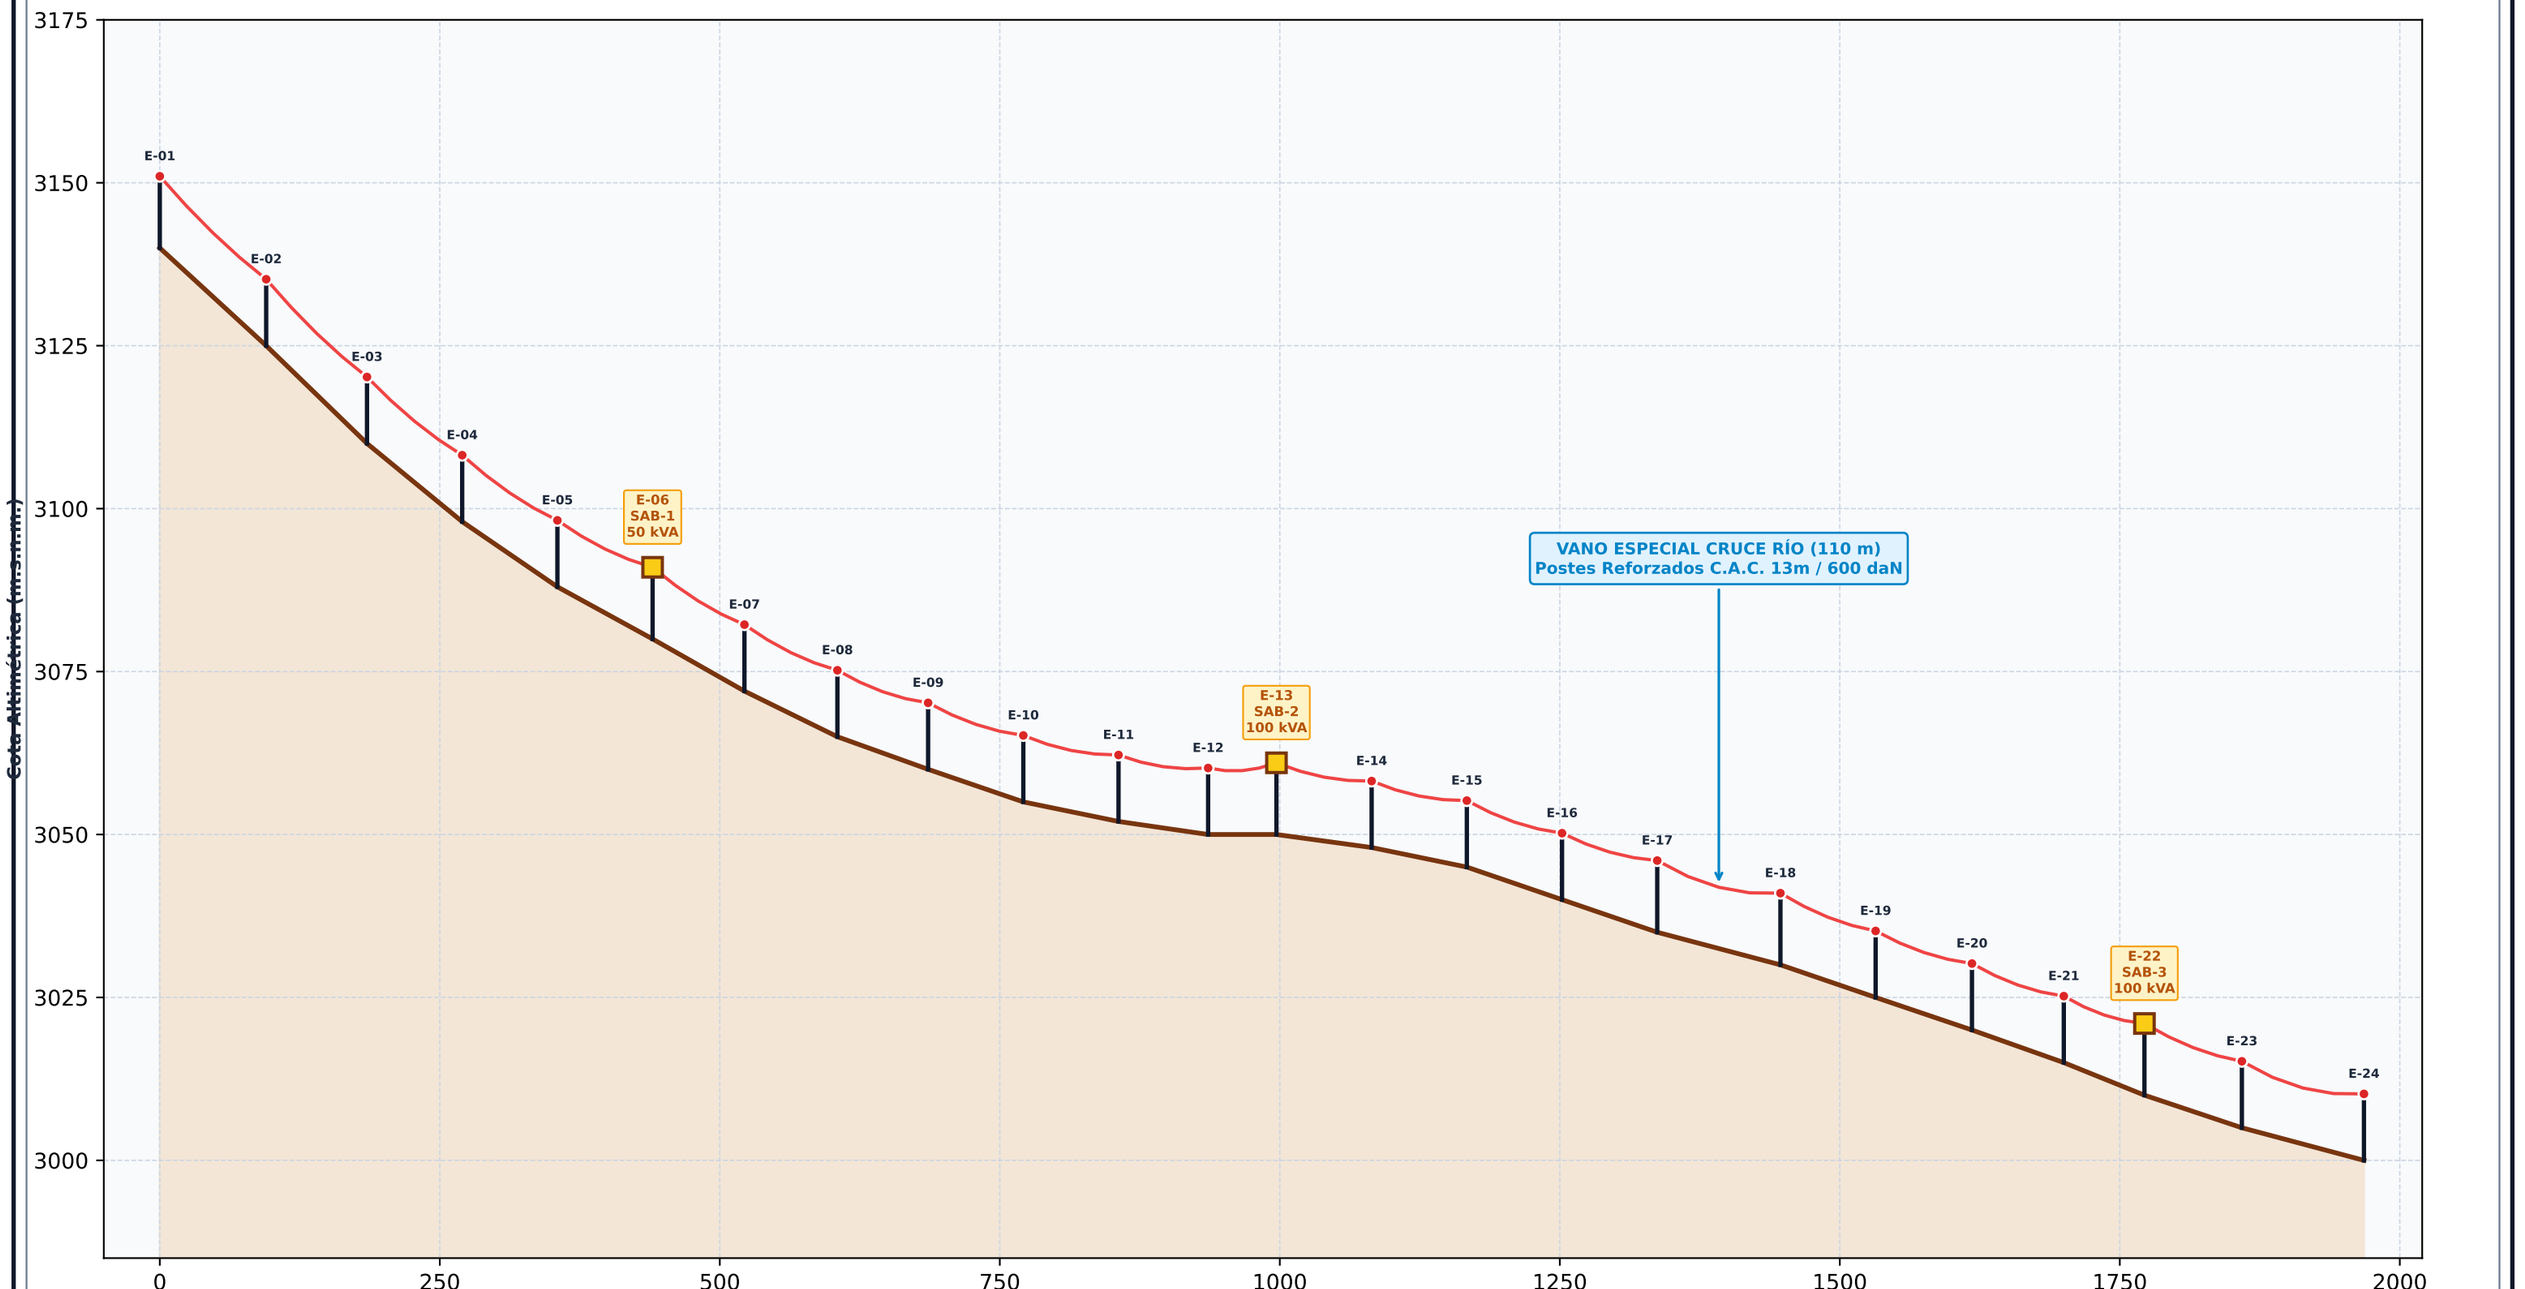

	E-01 PR-3	E-02 PS-3	E-03 PS-3	E-04 PA-3	E-05 PS-3	E-06 SAB-1	E-07 PS-3	E-08 PS-3	E-09 PA-3	E-10 PS-3	E-11 PS-3	E-12 PA-3	E-13 SAB-2	E-14 PS-3	E-15 PS-3	E-16 PA-3	E-17 PR-3	E-18 PR-3	E-19 PS-3	E-20 PS-3	E-21 PA-3	E-22 SAB-3	E-23 PS-3	E-24 PR-3
ESTRUCTURA / ARMADO																								
COTA TERRENO (m)	3110.0	3110.0	3110.0	3098.0	3088.0	3080.0	3072.0	3065.0	3060.0	3055.0	3052.0	3050.0	3050.0	3048.0	3045.0	3040.0	3035.0	3030.0	3025.0	3020.0	3015.0	3010.0	3005.0	3000.0
DISTANCIA ACUM. (m)	185	270	355	440	522	605	686	771	856	936	997	1082	1167	1252	1337	1447	1532	1618	1700	1772	1859	1968		
DISTANCIA PARCIAL (m)	85	85	85	82	83	81	85	85	80	61	85	85	85	85	110	85	86	82	72	87	109			

UNIVERSIDAD NACIONAL DEL ALTIPLANO — PUNO **FACULTAD DE INGENIERÍA MECÁNICA ELÉCTRICA (FIME)**	
ESCUELA PROFESIONAL DE INGENIERÍA MECÁNICA ELÉCTRICA **CURSO: INSTALACIONES ELÉCTRICAS II / REDES ELÉCTRICAS**	
EXPEDIENTE TÉCNICO: REDES ELÉCTRICAS MCH LIMBANI (200 kW) **DISTRITO DE LIMBANI — SANDIA — PUNO (3,050 m.s.n.m.)**	
PLANO: TRAZO Y PERFIL LONGITUDINAL MT 10 kV	
PROYECTISTA:	Br. Aquiles Taylor Ramos Yapo (Cód. 227368)
DOCENTE:	Docente FIME - UNA Puno
FECHA: Octubre 2026	**ESCALA:** H: 1:2000 | V: 1:200 — **LÁMINA:** PL-02